


CODE SECTIONS:

- FBC-B CH. 3 - OCCUPANCY CLASSIFICATION**
Group R-1 - Hotel (Transient: Occupancy of a dwelling unit or sleeping unit for not more than 30 days.)
Group R-2 - Apartment/Condo
- FBC-B §403.2 - ADDITIONAL INTERIOR EXIT STAIRWAY**
For buildings other than Group R-2 that are more than 420 feet (128 000 mm) in building height, one additional interior exit stairway meeting the requirements of Sections 1011 and 1023 shall be provided in addition to the minimum number of exits required by Section 1006.3. The total width of any combination of remaining interior exit stairways with one interior exit stairway removed shall be not less than the total width required by Section 1005.1. Scissor stairways shall not be considered the additional interior exit stairway required by this section.
Exception: An additional interior exit stairway shall not be required to be installed in buildings having elevators used for occupant self-evacuation in accordance with Section 3008.
- FBC-B §3008.1.2 ADDITIONAL EXIT STAIRWAY**
Where an additional means of egress is required in accordance with Section 403.5.2, an additional exit stairway shall not be required to be installed in buildings provided with occupant evacuation elevators complying with Section 3008.1.
- FBC-B §3008.6 OCCUPANT EVACUATION ELEVATOR LOBBY**
Occupant evacuation elevators shall open into an elevator lobby in accordance with Sections 3008.6.1 through 3008.6.6. Egress is permitted through the elevator lobby in accordance with Item 1 of Section 1016.2.
- FBC-B §3008.6.1 ACCESS TO INTERIOR EXIT STAIRWAY OR RAMP**
The occupant evacuation elevator lobby shall have direct access from the enclosed elevator lobby to an interior exit stairway or ramp.
Exceptions:
1.Access to an interior exit stairway or ramp shall be permitted to be through a protected path of travel that has a level of fire protection not less than the elevator lobby enclosure. The protected path shall be separated from the enclosed elevator lobby through an opening protected by a smoke and draft control assembly in accordance with Section 716.5.3.
2.Elevators that only service an open parking garage and the lobby of the building shall not be required to provide direct access in accordance with this section.

- FBC-B §3008.6.2 LOBBY ENCLOSURE**
The occupant evacuation elevator lobby shall be enclosed with a smoke barrier having a fire-resistance rating of not less than 1 hour, except that lobby doorways shall comply with Section 3008.6.3.
Exception: Enclosed occupant evacuation elevator lobbies are not required at the levels of exit discharge.
- FBC-B §3008.6.4 LOBBY SIZE**
Each occupant evacuation elevator lobby shall have minimum floor area as follows:
1.The occupant evacuation elevator lobby floor area shall accommodate, at 3 square feet (0.28 m2) per person, not less than 25 percent of the occupant load of the floor area served by the lobby.
2.The occupant evacuation elevator lobby floor area shall accommodate one wheelchair space of 30 inches by 48 inches (760 mm by 1220 mm) for each 50 persons, or portion thereof, of the occupant load of the floor area served by the lobby.
Exception: The size of lobbies serving multiple banks of elevators shall have the minimum floor area approved on an individual basis and shall be consistent with the building's fire safety and evacuation plan.
- FBC-B §3008.9 ELECTRICAL POWER**
The following features serving each occupant evacuation elevator shall be supplied by both normal power and Type 60/Class 2 Level 1 standby power:
1.Elevator equipment.
2.Ventilation and cooling equipment for elevator machine rooms, control rooms, machinery spaces and control spaces.
3.Elevator car lighting.


FBC	
EXIT STAIR A	TOTAL CAPACITY: 300 PEOPLE
STAIR WIDTH: 60"	OCCUPANCY FACTOR: 0.2
STAIR CAPACITY: 300 PEOPLE	
TOTAL CAPACITY:	OCCUPANCY FACTOR: 0.15
FBC: 300 X 2 = 600 PEOPLE	
DOOR CAPACITY CALCULATION IS BASED ON (3') OUT OF THE CURRENT DOOR WIDTH SHOWN.	

FFPC	
EXIT STAIR A	TOTAL CAPACITY: 220 PEOPLE
STAIR WIDTH: 60"	C = 146.7 + ((60 - 44) / 0.218)
STAIR CAPACITY: 220 PEOPLE	
TOTAL CAPACITY:	OCCUPANCY FACTOR: 0.2
FFPC: 225 X 2 = 450 PEOPLE	
DOOR CAPACITY CALCULATION IS BASED ON (3') OUT OF THE CURRENT DOOR WIDTH SHOWN.	

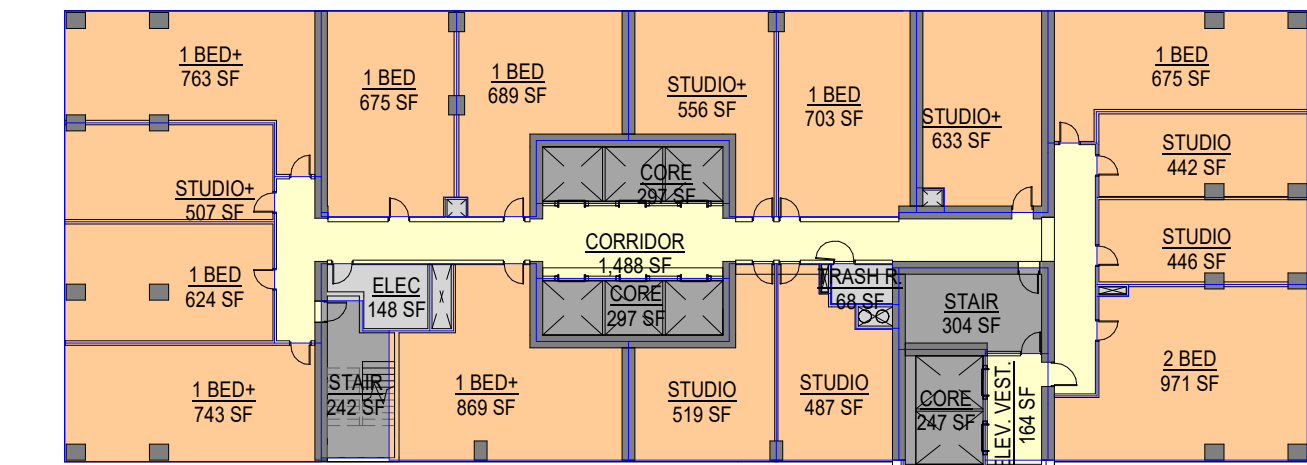


N. TYPE 1 STR LEVEL		
NAME	#	AREA
ELEC	1	148 SF
SHAFT	6	109 SF
TRASH R.	1	68 SF
CORRIDOR	1	1,488 SF
ELEV. VEST.	1	164 SF
CORE	3	840 SF
STAIR	2	546 SF
1 BED	5	3,365 SF
1 BED+	3	2,375 SF
2 BED	1	971 SF
STUDIO	4	1,893 SF
STUDIO+	3	1,696 SF
TOTAL:		13,664 SF

N. STR LEVELS 11 - 23		
NAME	#	AREA
ELEC	13	1,922 SF
SHAFT	78	1,423 SF
TRASH R.	13	882 SF
CORRIDOR	13	19,343 SF
ELEV. VEST.	13	2,131 SF
CORE	39	10,921 SF
STAIR	26	7,098 SF
1 BED	65	43,749 SF
1 BED+	39	30,875 SF
2 BED	13	12,619 SF
STUDIO	52	24,612 SF
STUDIO+	39	22,053 SF
TOTAL:		177,629 SF

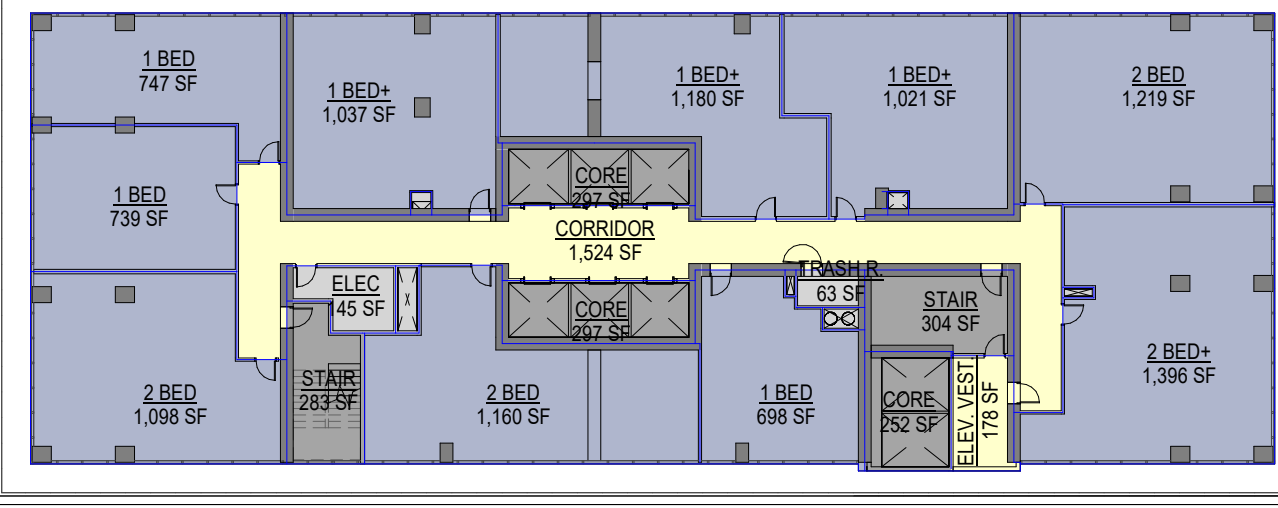


N. LIFESTYLE TYPE 1		
NAME	#	AREA
ELEC	1	145 SF
SHAFT	6	101 SF
TRASH R.	1	63 SF
CORRIDOR	1	1,524 SF
ELEV. VEST.	1	178 SF
CORE	3	845 SF
STAIR	2	587 SF
1 BED	3	2,184 SF
1 BED+	3	2,328 SF
2 BED	3	3,478 SF
2 BED+	1	1,396 SF
TOTAL:		13,739 SF

N. LIFESTYLE LVL 38 - 50		
NAME	#	AREA
ELEC	13	1,882 SF
SHAFT	78	1,308 SF
TRASH R.	13	818 SF
CORRIDOR	13	19,809 SF
ELEV. VEST.	13	2,318 SF
CORE	39	10,989 SF
STAIR	26	7,633 SF
1 BED	39	28,391 SF
1 BED+	39	42,096 SF
2 BED	39	45,210 SF
2 BED+	13	18,147 SF
TOTAL:		178,602 SF

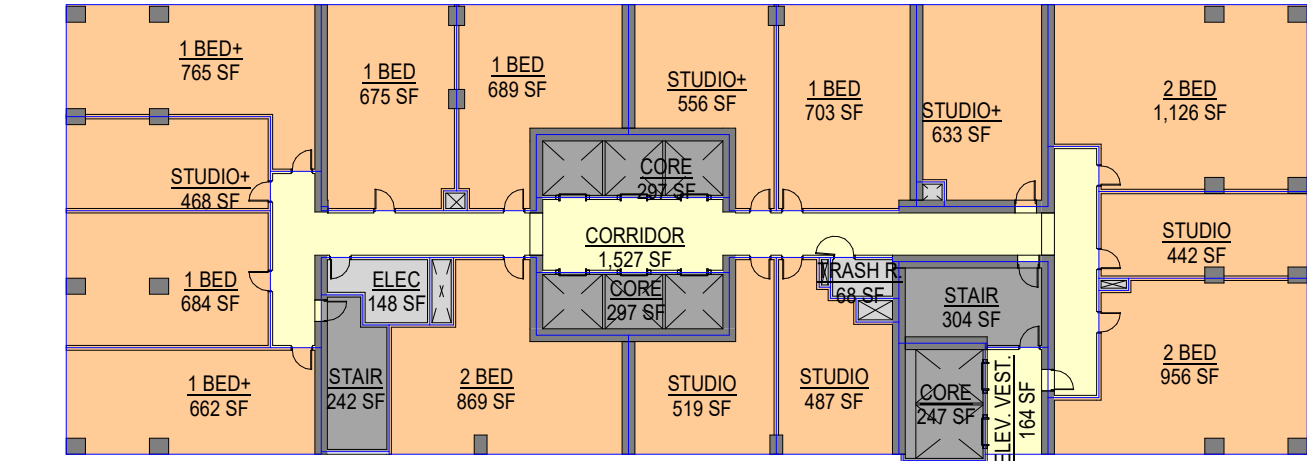


N. TYPE 2 STR LEVEL		
NAME	#	AREA
ELEC	1	148 SF
SHAFT	6	109 SF
TRASH R.	1	68 SF
CORRIDOR	1	1,527 SF
ELEV. VEST.	1	164 SF
CORE	3	840 SF
STAIR	2	546 SF
1 BED	4	2,751 SF
1 BED+	2	1,427 SF
2 BED	3	2,952 SF
STUDIO	3	1,448 SF
STUDIO+	3	1,657 SF
TOTAL:		13,636 SF

N. STR LEVELS 24 - 28		
NAME	#	AREA
ELEC	5	739 SF
SHAFT	30	545 SF
TRASH R.	5	339 SF
CORRIDOR	5	7,635 SF
ELEV. VEST.	5	819 SF
CORE	15	4,201 SF
STAIR	10	2,730 SF
1 BED	20	13,754 SF
1 BED+	10	7,133 SF
2 BED	15	14,760 SF
STUDIO	15	7,239 SF
STUDIO+	15	8,287 SF
TOTAL:		68,181 SF

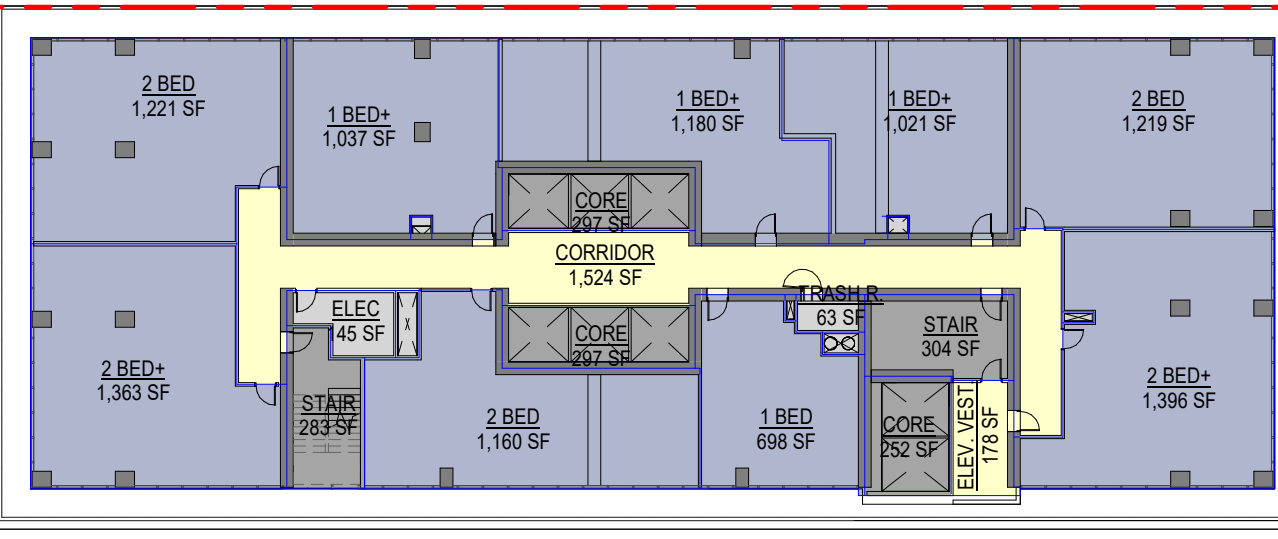


N. LIFESTYLE TYPE 2		
NAME	#	AREA
ELEC	1	145 SF
SHAFT	6	101 SF
TRASH R.	1	63 SF
CORRIDOR	1	1,524 SF
ELEV. VEST.	1	178 SF
CORE	3	845 SF
STAIR	2	587 SF
1 BED	1	698 SF
1 BED+	3	3,238 SF
2 BED	3	3,600 SF
2 BED+	2	2,759 SF
TOTAL:		13,739 SF

N. LIFESTYLE LVL 51 - 53		
NAME	#	AREA
ELEC	3	434 SF
SHAFT	18	302 SF
TRASH R.	3	189 SF
CORRIDOR	3	4,571 SF
ELEV. VEST.	3	535 SF
CORE	9	2,536 SF
STAIR	6	1,761 SF
1 BED	3	2,094 SF
1 BED+	9	9,714 SF
2 BED	9	10,801 SF
2 BED+	6	8,277 SF
TOTAL:		41,216 SF

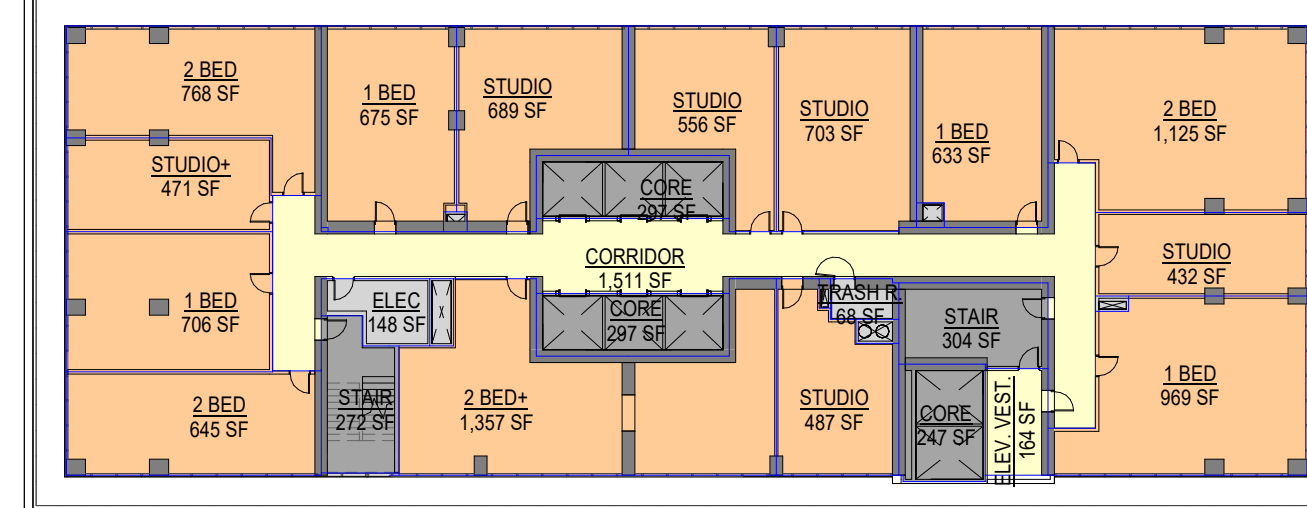


N. TYPE 3 STR LEVEL		
NAME	#	AREA
ELEC	1	148 SF
SHAFT	6	113 SF
TRASH R.	1	68 SF
CORRIDOR	1	1,511 SF
ELEV. VEST.	1	164 SF
CORE	3	840 SF
STAIR	2	576 SF
1 BED	4	2,982 SF
2 BED	3	2,538 SF
2 BED+	1	1,357 SF
STUDIO	5	2,868 SF
STUDIO+	1	471 SF
TOTAL:		13,636 SF

N. STR LEVELS 29 - 37		
NAME	#	AREA
ELEC	9	1,331 SF
SHAFT	54	1,014 SF
TRASH R.	9	611 SF
CORRIDOR	9	13,598 SF
ELEV. VEST.	9	1,475 SF
CORE	27	7,561 SF
STAIR	18	5,186 SF
1 BED	36	26,840 SF
2 BED	27	22,839 SF
2 BED+	9	12,214 SF
STUDIO	45	25,811 SF
STUDIO+	9	4,242 SF
TOTAL:		122,721 SF

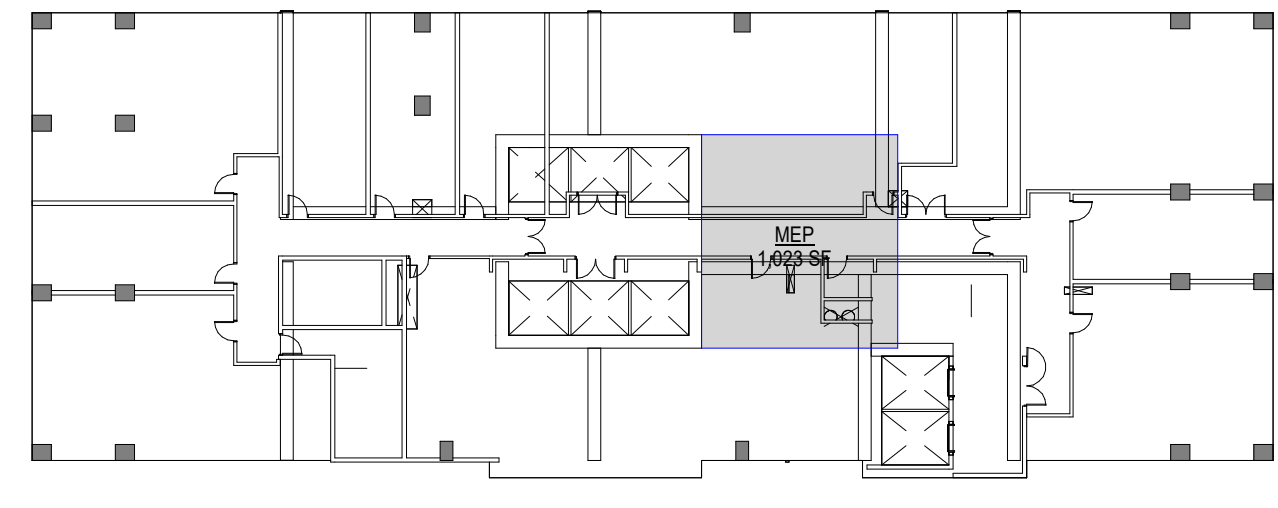

N. STR LEVEL 54				
NAME	#	AREA	OCC. FACTOR	OCC. LOAD
MEP	1	1,023 SF		0
TOTAL:		1,023 SF		0

N - LEVEL 54

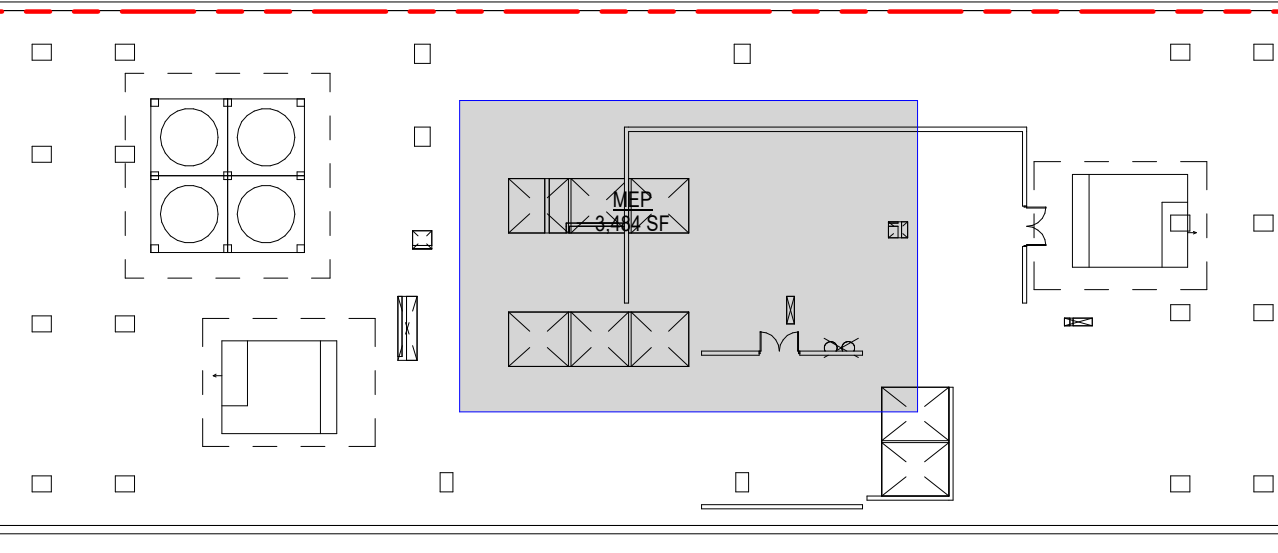


N - LEVEL 55 - ROOF

AREA ANALYSIS NORTH TOWER

BLOCK C


A.004

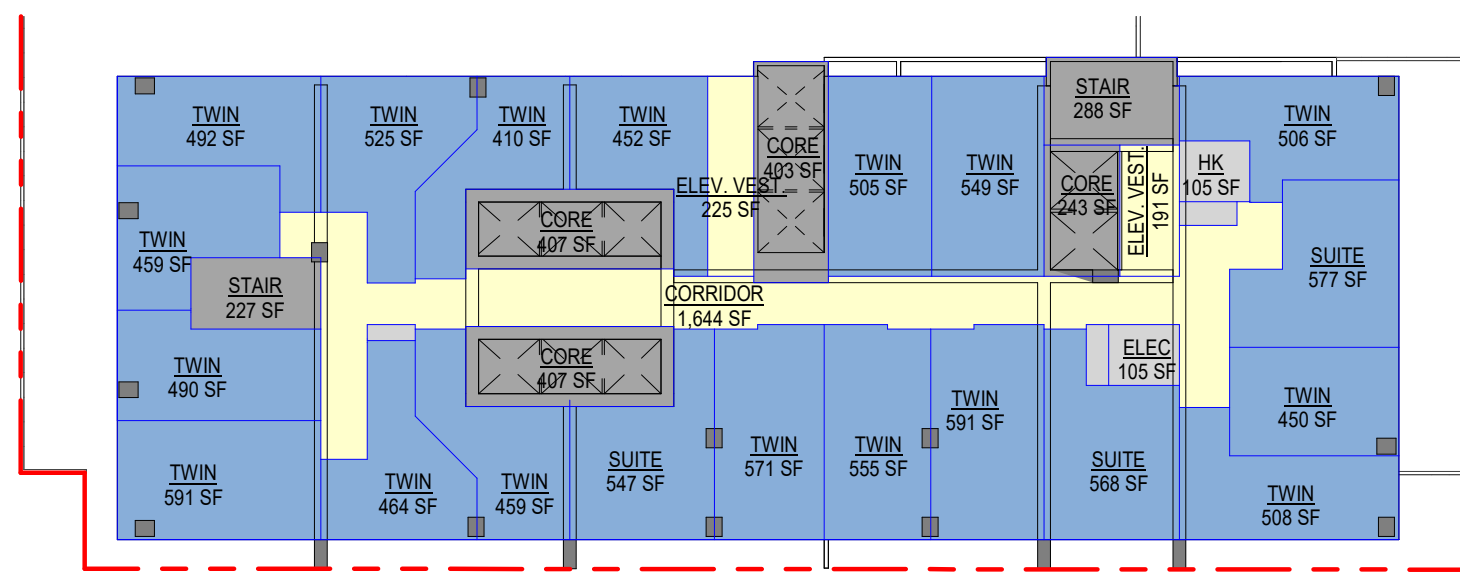

S - LEVELS 11 - 14 | HOTEL TYPE 1
1 / A.005 | 1" = 30'-0"

S. HOTEL TYPE 1				
NAME	#	AREA	OCC. FACTOR	OCC. LOAD
ELEC	1	105 SF	0	0
HK	1	105 SF	0	0
SHAFT	3	86 SF	0	0
CORRIDOR	1	1,644 SF	0	0
ELEV. VEST.	2	416 SF	0	0
CORE	4	1,459 SF	0	0
STAIR	2	515 SF	0	0
SUITE	3	1,692 SF	0	0
TWIN	17	8,576 SF	0	0
TOTAL:		14,598 SF		0


S. HOTEL LEVELS 11 - 14		
NAME	#	AREA
ELEC	4	421 SF
HK	4	418 SF
SHAFT	12	342 SF
CORRIDOR	4	6,578 SF
ELEV. VEST.	8	1,664 SF
CORE	16	5,836 SF
STAIR	8	2,062 SF
SUITE	12	6,768 SF
TWIN	68	34,305 SF
TOTAL:		58,393 SF

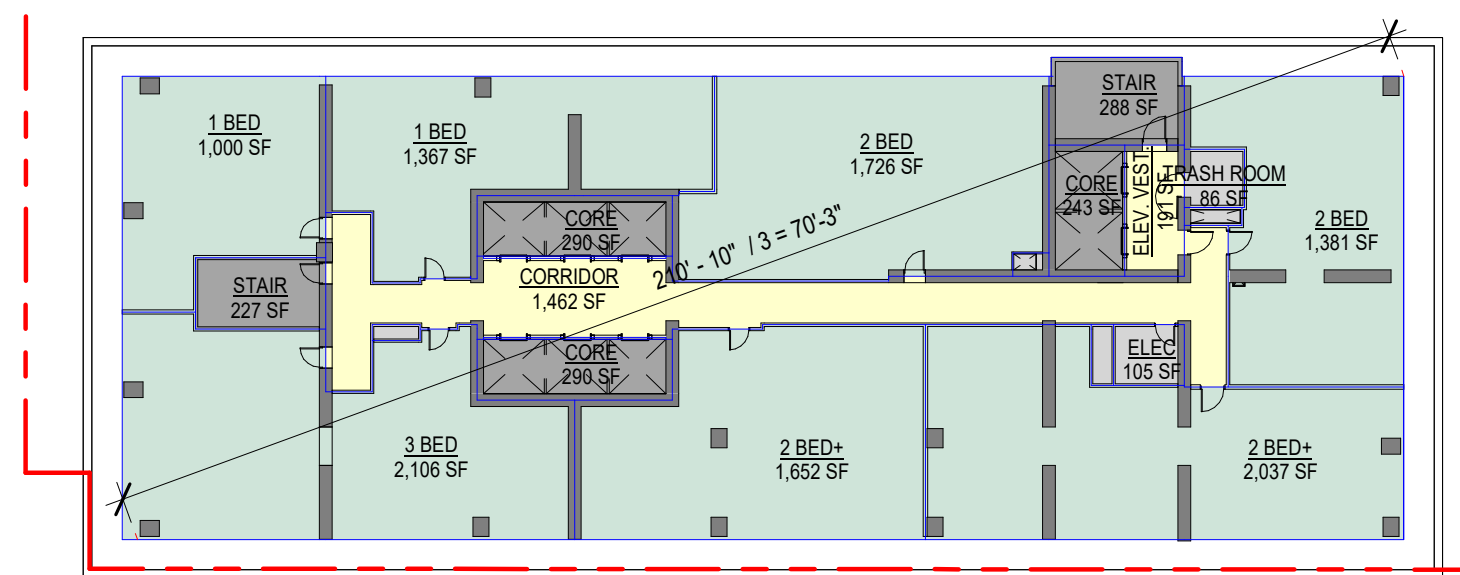

S - LEVELS 37 - 42 | BRANDED RESI SMALL
7 / A.005 | 1" = 30'-0"

S. BRANDED RESI SMALL				
NAME	#	AREA	OCC. FACTOR	OCC. LOAD
ELEC	1	105 SF	0	0
SHAFT	4	98 SF	0	0
TRASH ROOM	1	86 SF	0	0
1 BED	2	2,367 SF	0	0
2 BED	2	3,106 SF	0	0
2 BED+	2	3,689 SF	0	0
3 BED	1	2,106 SF	0	0
CORRIDOR	1	1,462 SF	0	0
ELEV. VEST.	1	191 SF	0	0
CORE	3	823 SF	0	0
STAIR	2	515 SF	0	0
TOTAL:		14,549 SF		0

S. RESI. LEVELS 37 - 42		
NAME	#	AREA
ELEC	6	632 SF
SHAFT	24	589 SF
TRASH ROOM	6	514 SF
1 BED	12	14,204 SF
2 BED	12	18,638 SF
2 BED+	12	22,134 SF
3 BED	6	12,638 SF
CORRIDOR	6	8,772 SF
ELEV. VEST.	6	1,148 SF
CORE	18	4,936 SF
STAIR	12	3,093 SF
TOTAL:		87,296 SF

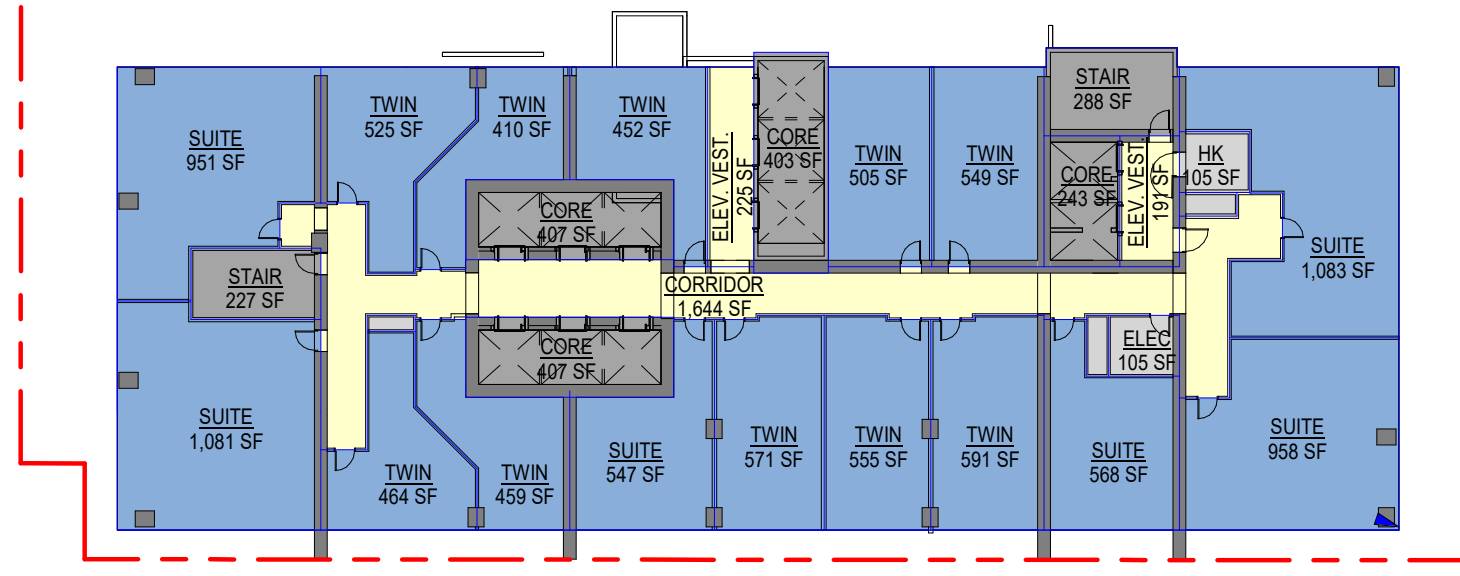


S - LEVELS 15 - 17 | HOTEL TYPE 2
2 / A.005 | 1" = 30'-0"

S. HOTEL TYPE 2				
NAME	#	AREA	OCC. FACTOR	OCC. LOAD
ELEC	1	105 SF	0	0
HK	1	105 SF	0	0
SHAFT	3	86 SF	0	0
CORRIDOR	1	1,644 SF	0	0
ELEV. VEST.	2	416 SF	0	0
CORE	4	1,459 SF	0	0
STAIR	2	515 SF	0	0
SUITE	6	5,188 SF	0	0
TWIN	10	5,080 SF	0	0
TOTAL:		14,598 SF		0

S. HOTEL LEVELS 15 - 17		
NAME	#	AREA
ELEC	3	316 SF
HK	3	314 SF
SHAFT	9	257 SF
CORRIDOR	3	4,933 SF
ELEV. VEST.	6	1,248 SF
CORE	12	4,377 SF
STAIR	6	1,546 SF
SUITE	18	15,564 SF
TWIN	30	15,240 SF
TOTAL:		43,795 SF


S. HOTEL UNIT MIX				
NAME	TOTAL AREA	AREA: MIN. - MAX.	%	#
SUITE	22,333 SF	547 SF ... 1,083 SF	31.07%	30
TWIN	49,545 SF	410 SF ... 591 SF	68.93%	98
TOTAL:	71,878 SF		100.00%	128

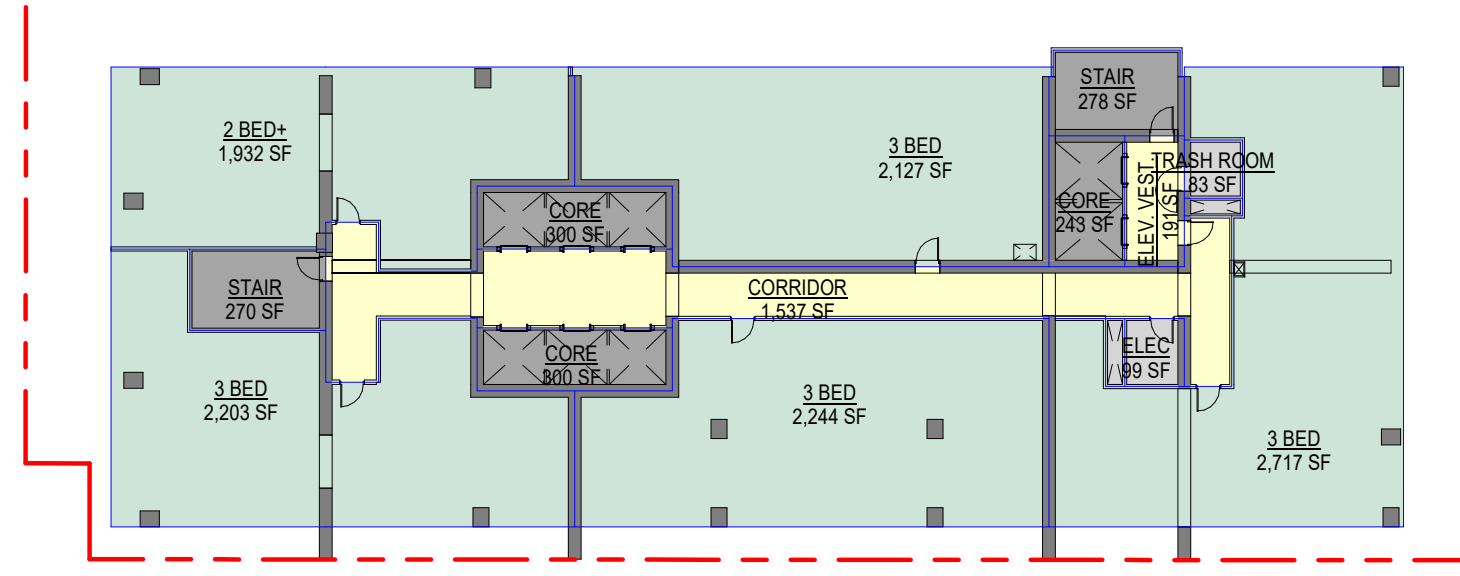

S - LEVELS 43 - 49 | BRANDED RESI LARGE
5 / A.005 | 1" = 30'-0"

S. BRANDED RESI SMALL				
NAME	#	AREA	OCC. FACTOR	OCC. LOAD
ELEC	1	99 SF	0	0
SHAFT	2	57 SF	0	0
TRASH ROOM	1	83 SF	0	0
2 BED+	1	1,932 SF	0	0
3 BED	4	9,291 SF	0	0
CORRIDOR	1	1,537 SF	0	0
ELEV. VEST.	1	191 SF	0	0
CORE	3	843 SF	0	0
STAIR	2	548 SF	0	0
TOTAL:		14,581 SF		0


S. RESI. LEVELS 43 - 49		
NAME	#	AREA
ELEC	7	695 SF
SHAFT	14	400 SF
TRASH ROOM	7	578 SF
2 BED+	7	13,522 SF
3 BED	28	65,037 SF
CORRIDOR	7	10,758 SF
ELEV. VEST.	7	1,339 SF
CORE	21	5,901 SF
STAIR	14	3,838 SF
TOTAL:		102,068 SF

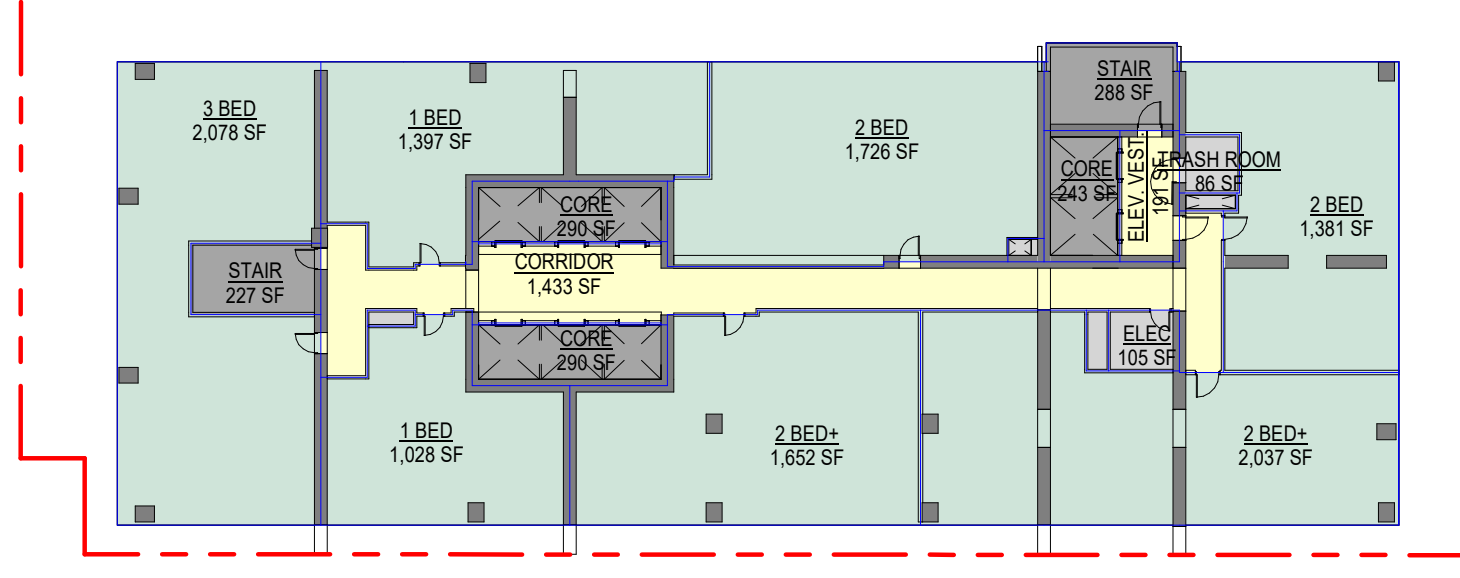

S - LEVELS 18 - 34 | BRANDED RESI SMALL
4 / A.005 | 1" = 30'-0"


S. BRANDED RESI SMALL				
NAME	#	AREA	OCC. FACTOR	OCC. LOAD
ELEC	1	105 SF	0	0
SHAFT	4	98 SF	0	0
TRASH ROOM	1	86 SF	0	0
1 BED	2	2,425 SF	0	0
2 BED	2	3,106 SF	0	0
2 BED+	2	3,689 SF	0	0
3 BED	1	2,078 SF	0	0
CORRIDOR	1	1,433 SF	0	0
ELEV. VEST.	1	191 SF	0	0
CORE	3	823 SF	0	0
STAIR	2	515 SF	0	0
TOTAL:		14,549 SF		0

S. RESI. LEVELS 18 - 34		
NAME	#	AREA
ELEC	17	1,789 SF
SHAFT	68	1,668 SF
TRASH ROOM	17	1,457 SF
1 BED	34	41,223 SF
2 BED	34	52,807 SF
2 BED+	34	62,714 SF
3 BED	17	35,321 SF
CORRIDOR	17	24,359 SF
ELEV. VEST.	17	3,253 SF
CORE	51	13,985 SF
STAIR	34	8,763 SF
TOTAL:		247,338 SF

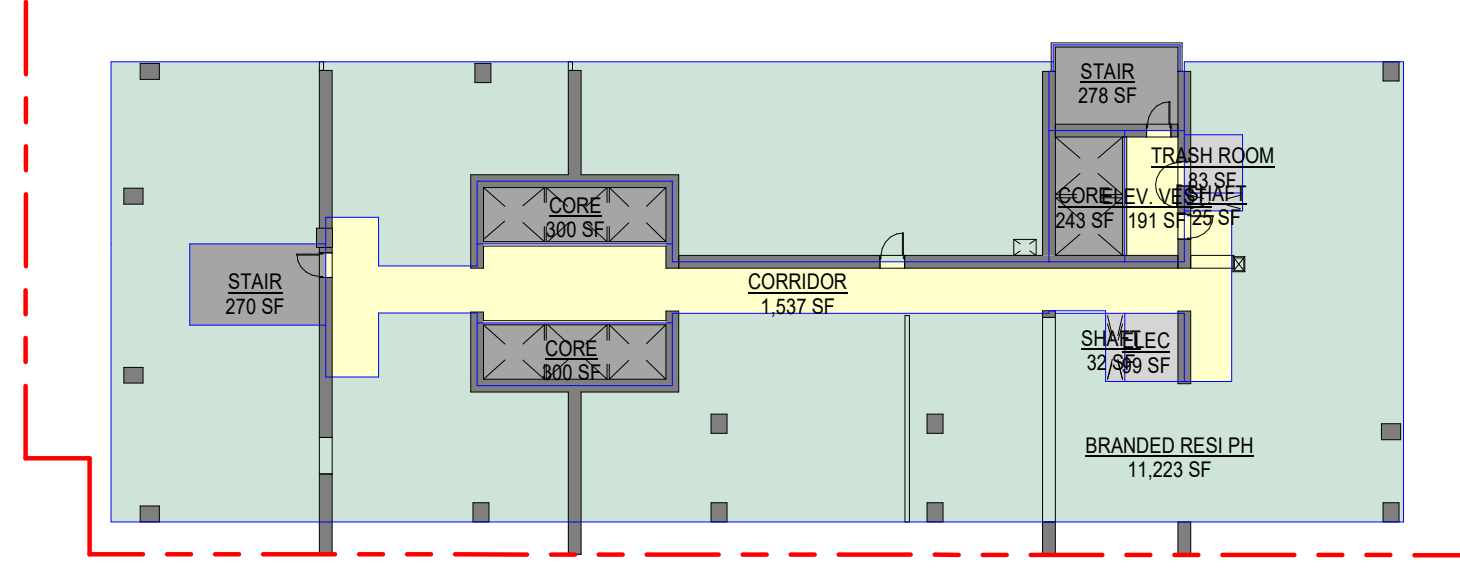


S - LEVEL 50 - BRANDED RESI PH
10 / A.005 | 1" = 30'-0"

S. RESI. LEVEL 50		
NAME	#	AREA
ELEC	1	99 SF
SHAFT	2	57 SF
TRASH ROOM	1	83 SF
BRANDED RESI PH	1	11,223 SF
CORRIDOR	1	1,537 SF
ELEV. VEST.	1	191 SF
CORE	3	843 SF
STAIR	2	548 SF
TOTAL:		14,581 SF

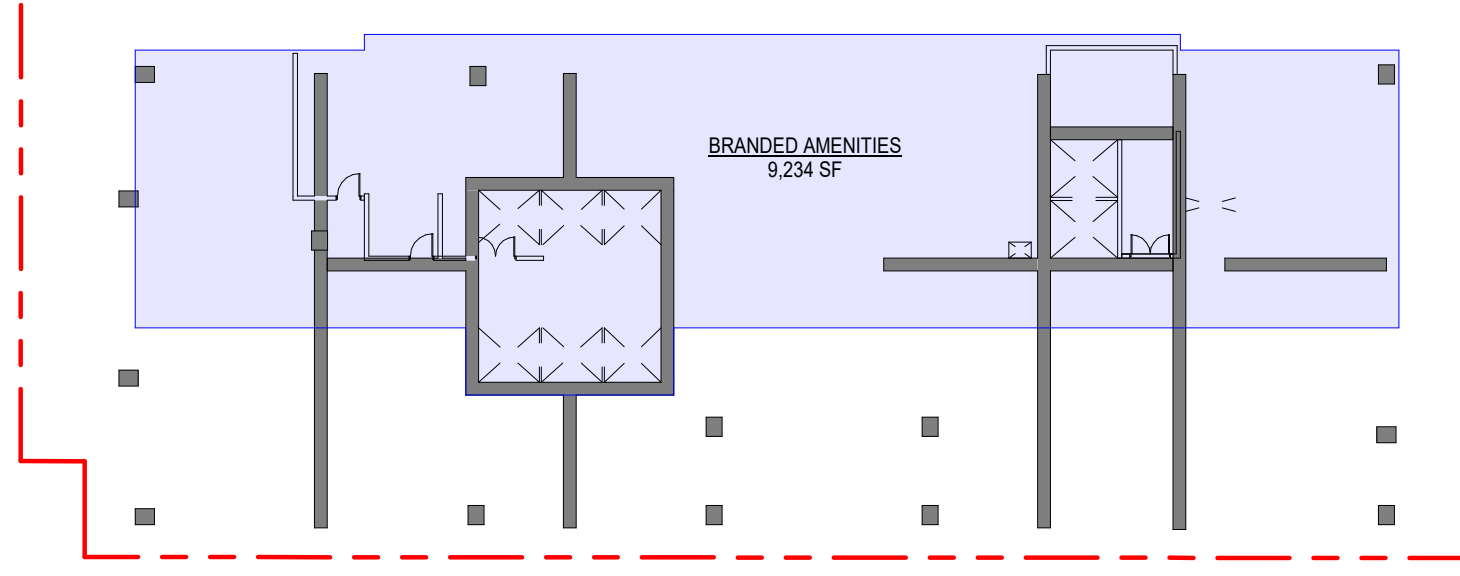


S - LEVEL 35 | BRANDED AMENITIES
6 / A.005 | 1" = 30'-0"

S. RESI. LEVEL 35				
NAME	#	AREA	OCC. FACTOR	OCC. LOAD
BRANDED AMENITIES	1	9,234 SF		0
TOTAL:		9,234 SF		0

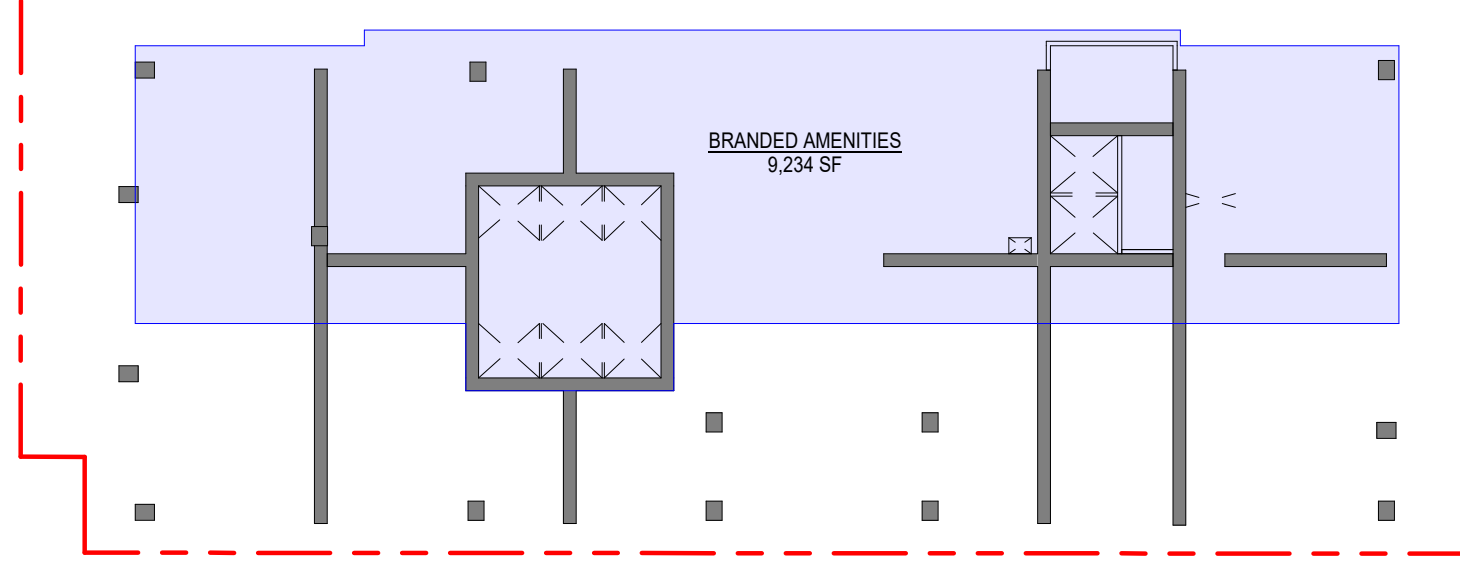

S. RESI. LEVEL 36				
NAME	#	AREA	OCC. FACTOR	OCC. LOAD
BRANDED AMENITIES	1	9,234 SF		0
TOTAL:		9,234 SF		0

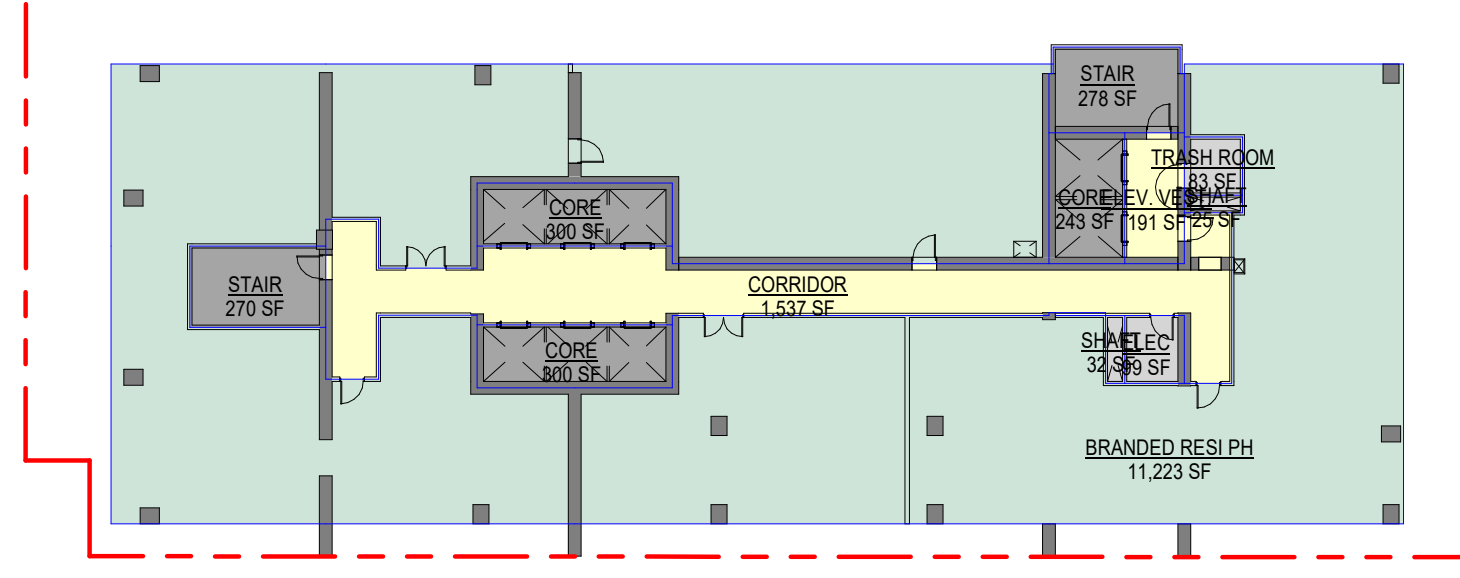

S - LEVEL 51 - BRANDED RESI PH
11 / A.005 | 1" = 30'-0"

S. RESI. LEVEL 51		
NAME	#	AREA
ELEC	1	99 SF
SHAFT	2	57 SF
TRASH ROOM	1	83 SF
BRANDED RESI PH	1	11,223 SF
CORRIDOR	1	1,537 SF
ELEV. VEST.	1	191 SF
CORE	3	843 SF
STAIR	2	548 SF
TOTAL:		14,581 SF

S. RESI. LEVEL 52		
NAME	#	AREA
MEP	1	1,050 SF
TOTAL:		1,050 SF

S. BRANDED RESI UNIT MIX				
NAME	TOTAL AREA	AREA: MIN. - MAX.	%	#
1 BED	55,427 SF	1,000 SF ... 1,397 SF	15.37%	46
2 BED	71,445 SF	1,381 SF ... 1,726 SF	19.81%	46
2 BED+	98,370 SF	1,652 SF ... 2,037 SF	27.27%	53
3 BED	112,996 SF	2,078 SF ... 2,717 SF	31.33%	51
BRANDED RESI PH	22,445 SF	11,223 SF	6.22%	2
TOTAL:	360,683 SF		100.00%	198

S. RESI. LEVEL 53		
NAME	#	AREA
MEP	1	3,080 SF
TOTAL:		3,080 SF

S - LEVEL 36 | BRANDED AMENITIES
3 / A.005 | 1" = 30'-0"